



Site View

CODE	SUITABILITY DESCRIPTION
------	-------------------------

STATUS	PURPOSE OF ISSUE

www.autodesk.com/revit

TITLE

Site View

CLIENT

Leeds City Council

DRAWN BY T Hermolle	CHECKED BY Checker	DATE 01/23/07
SCALE (@ A1) 1 : 500		PROJECT NUMBER Project Number
DRAWING NUMBER A100		REV



Ground Floor View

1 : 200

Rev	Description	Date

CODE SUITABILITY DESCRIPTION

STATUS PURPOSE OF ISSUE

AUTODESK
www.autodesk.com/revit

PROJECT
**MSATD Major Design
Project**


TITLE
Ground Floor View

CLIENT
Leeds City Council

DRAWN BY T Hermolle CHECKED BY Checker DATE 12/12/25

SCALE (@ A1) 1 : 200 PROJECT NUMBER Project Number

DRAWING NUMBER A102 REV

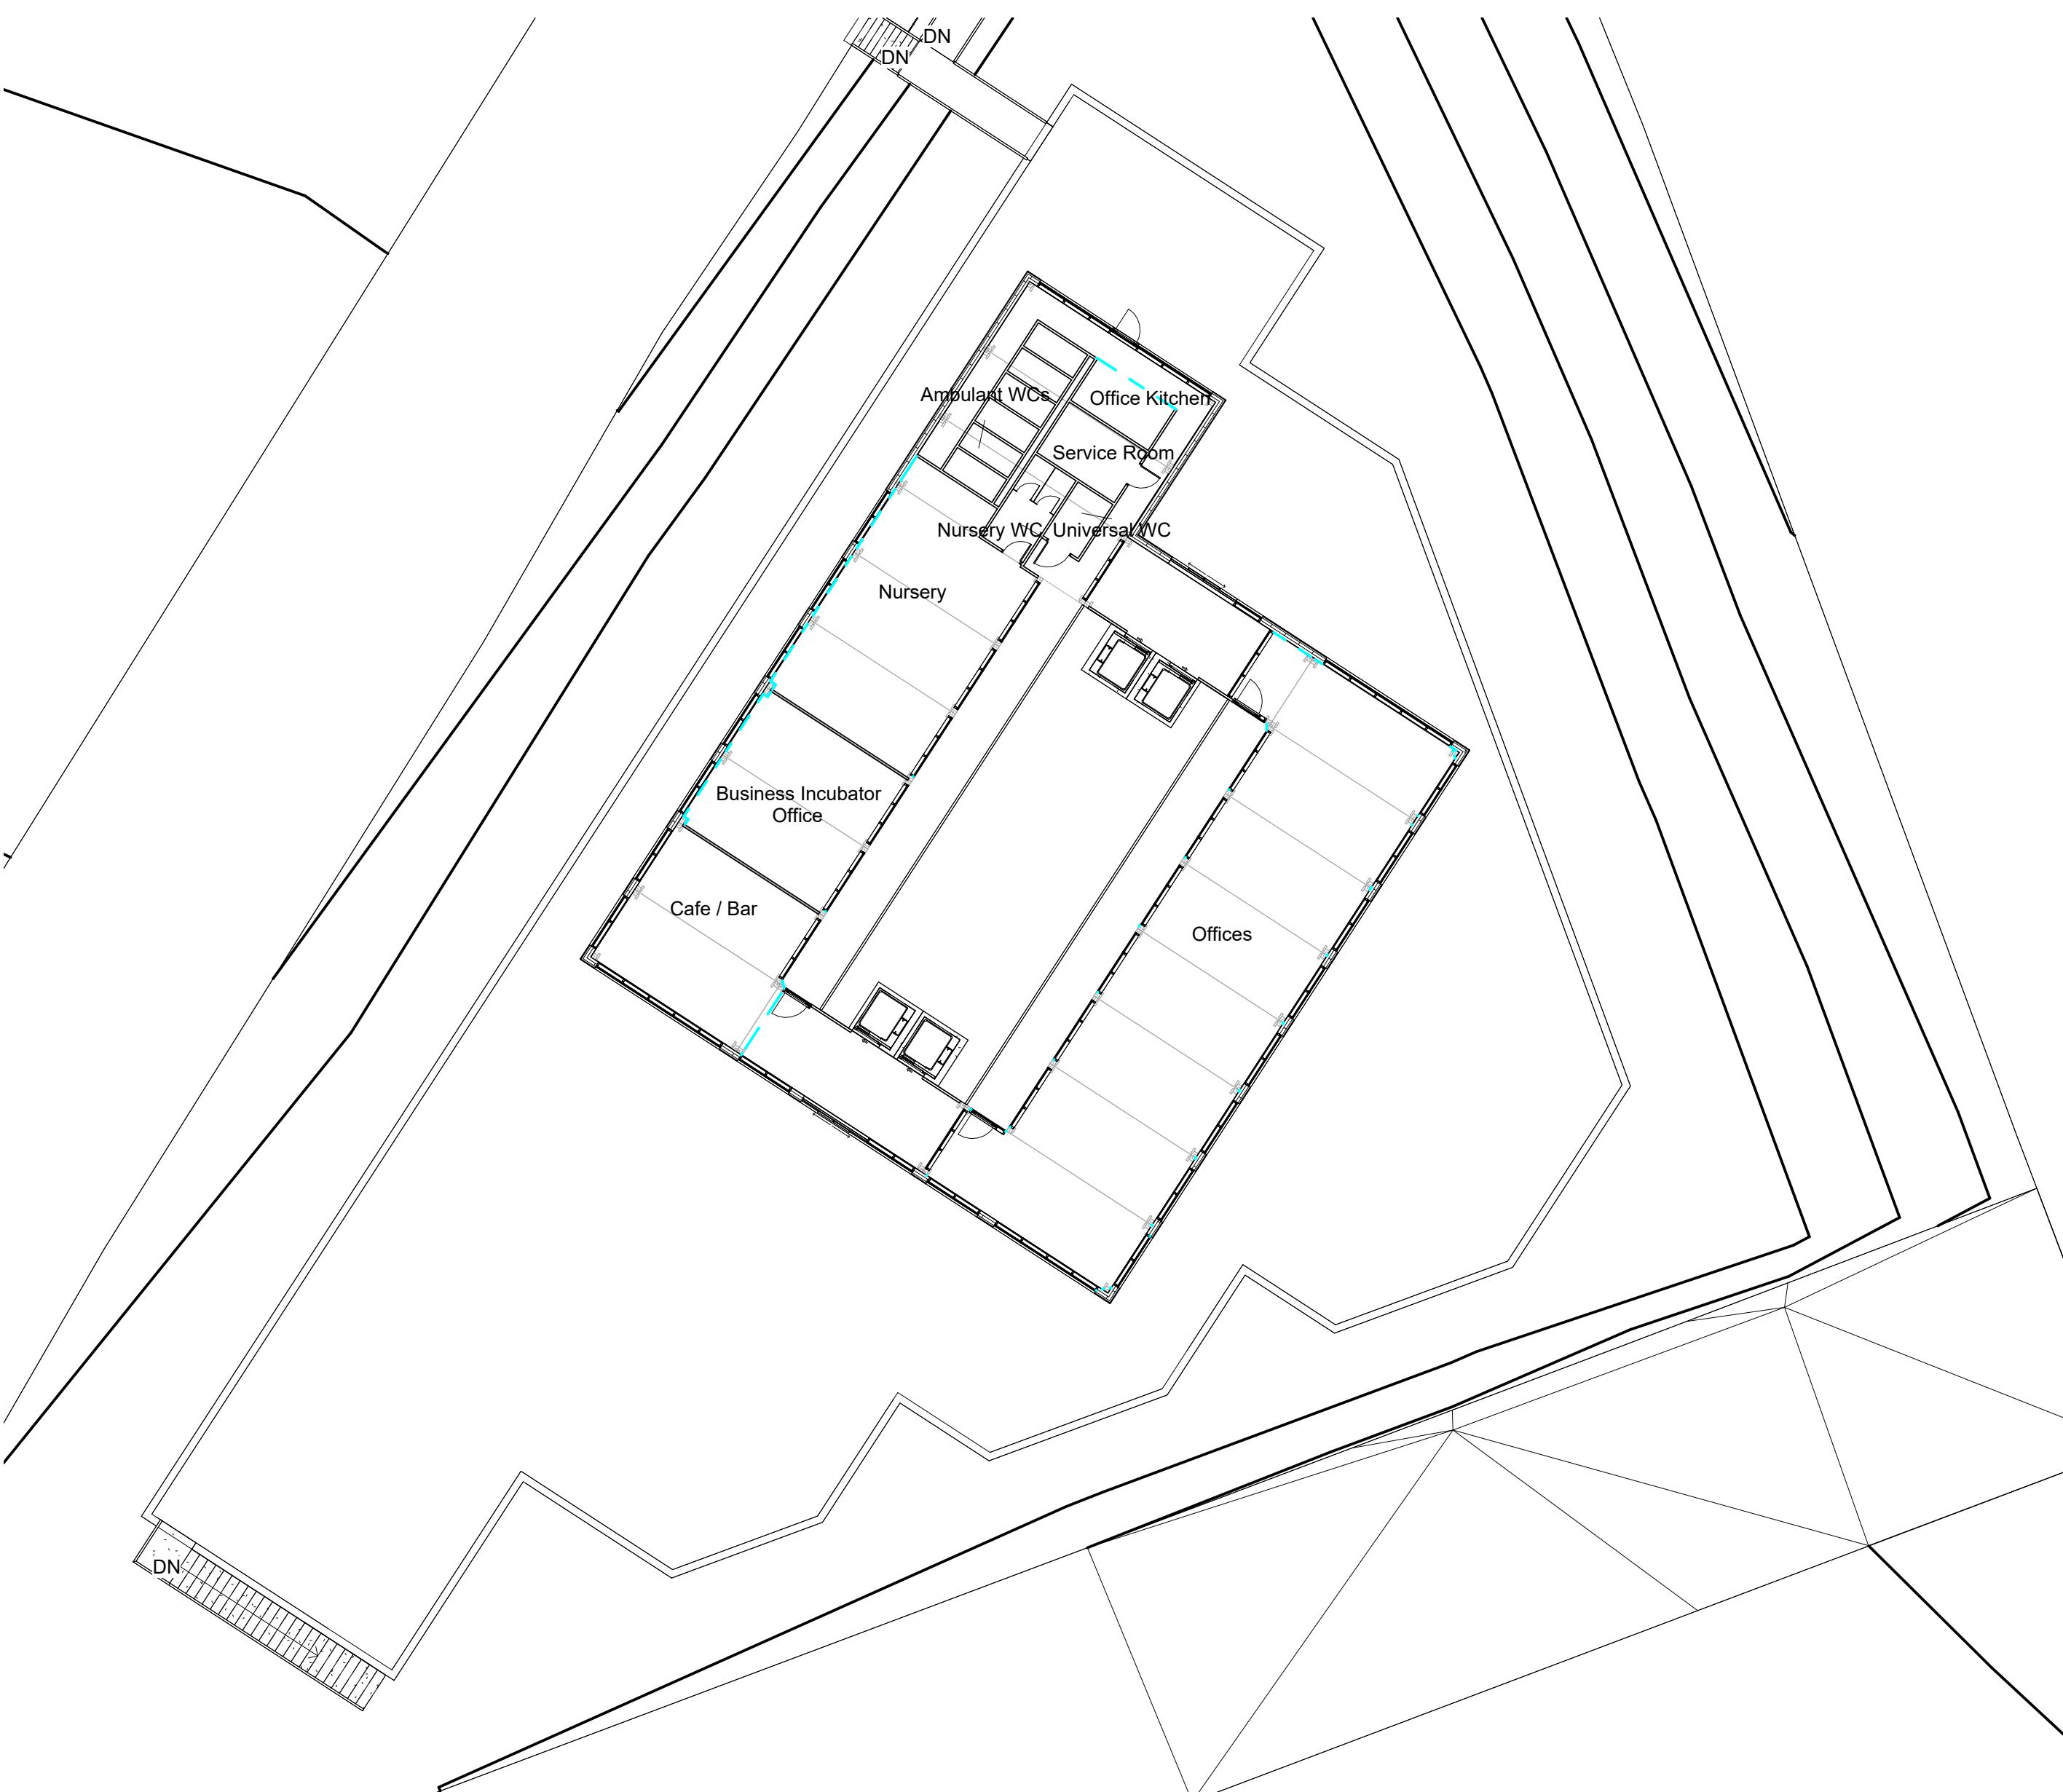

First Floor View

1 : 200

CODE	SUITABILITY DESCRIPTION
------	-------------------------

S	PURPOSE OF ISSUE
---	------------------

MSATD Major Design Project

First Floor View

CLIENT

Leeds City Council

DRAWN BY T Hermolle	CHECKED BY Checker	DATE 12/12/25
SCALE (@ A1) 1 : 200	PROJECT NUMBER Project Number	
DRAWING NUMBER A103	REV	



Vernon St
1 : 200



4 **South West**
1 : 200



2 Cookridge St
1 : 200



3 Woodhouse Lane
1 : 200

CODE	SUITABILITY DESCRIPTION
------	-------------------------

STATUS	PURPOSE OF ISSUE
--------	------------------

 AUTODESK

PROJECT


MSATD Major Design Project

Elevations


CLIENT

Leeds City Council

DRAWN BY T Hermolle	CHECKED BY Checker	DATE 12/12/25
SCALE (@ A1) 1 : 200	PROJECT NUMBER Project Number	
DRAWING NUMBER A104	REV	

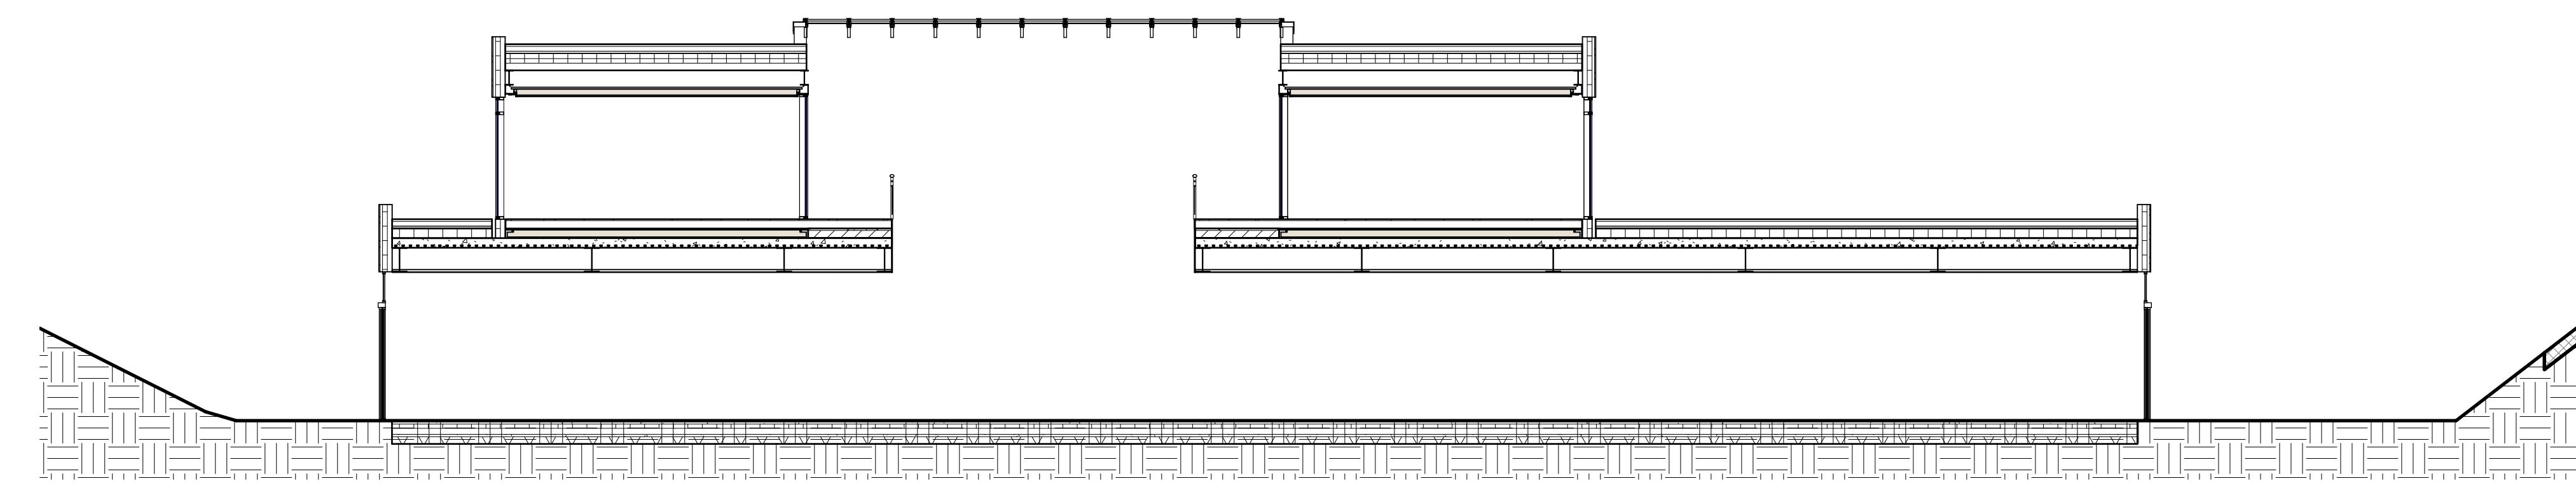

NW-SE Section

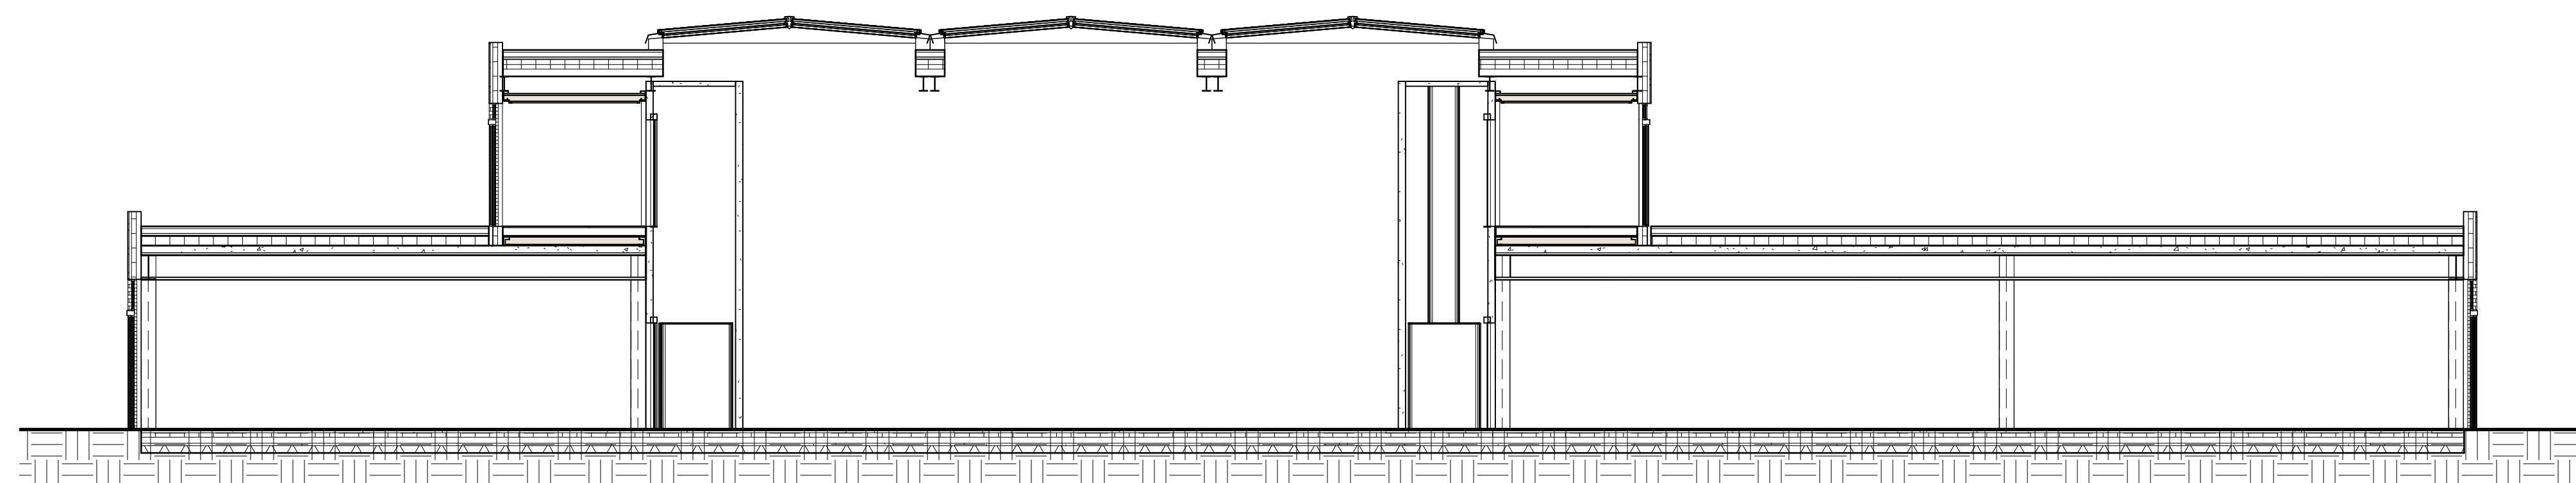

NE-SW Section

CODE	SUITABILITY DESCRIPTION
STATUS	PURPOSE OF ISSUE

 AUTODESK


www.autodesk.com/revit

Sections


CLIENT

Leeds City Council

DRAWN BY T Hermolle	CHECKED BY Checker	DATE 12/12/25
SCALE (@ A1) 1 : 100	PROJECT NUMBER Project Number	
DRAWING NUMBER A105	REV	

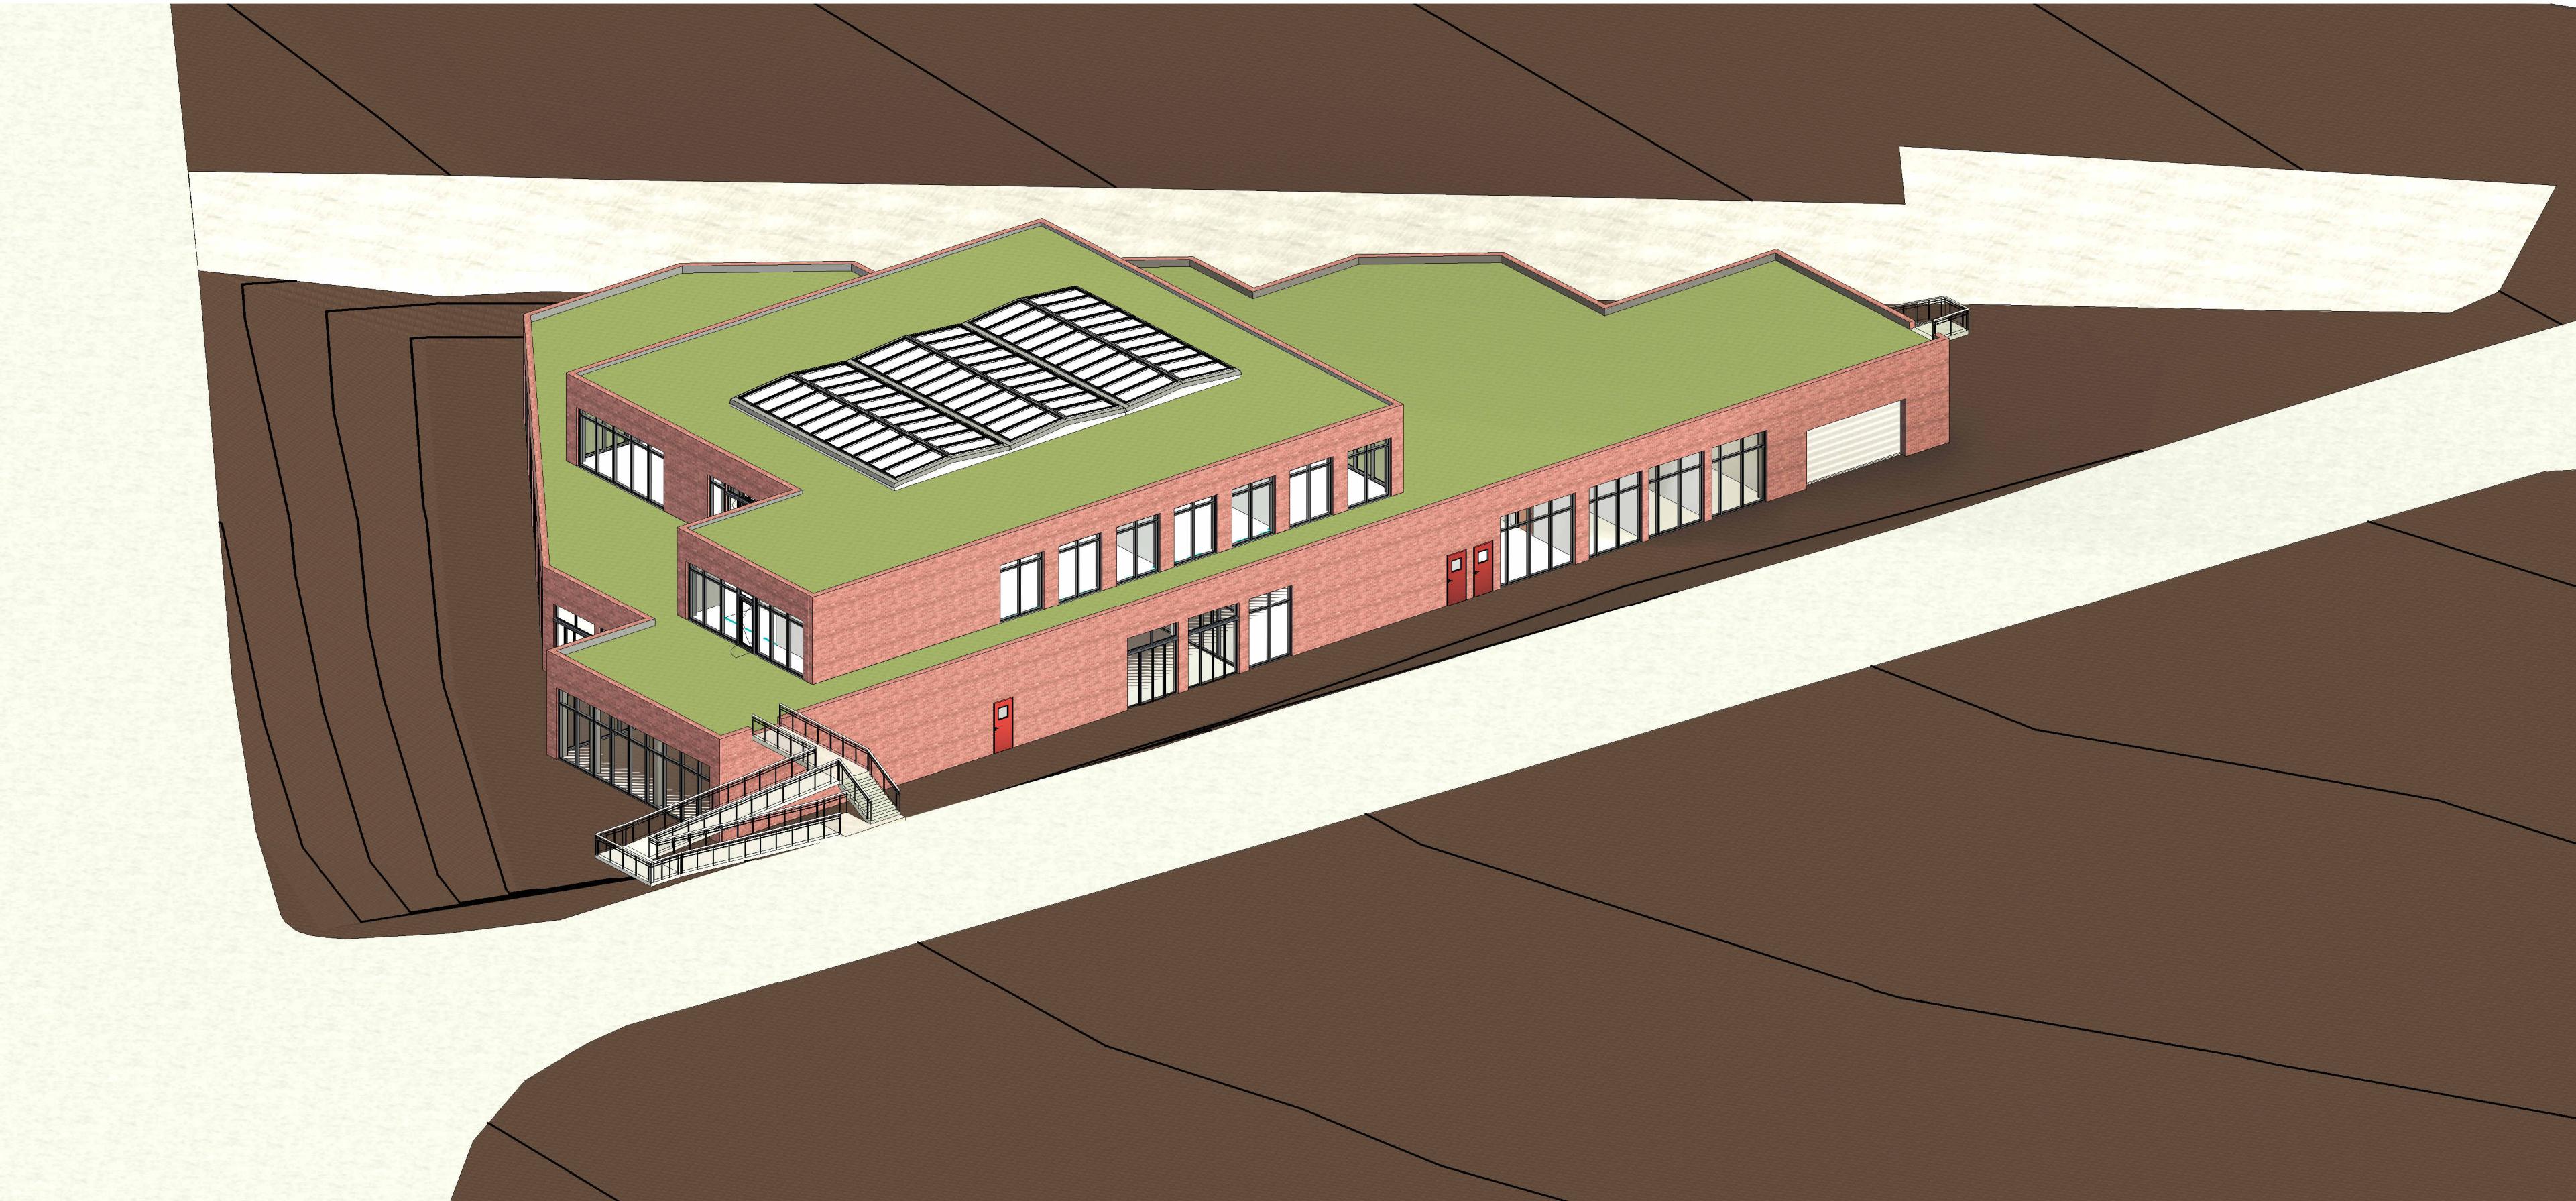

3D North

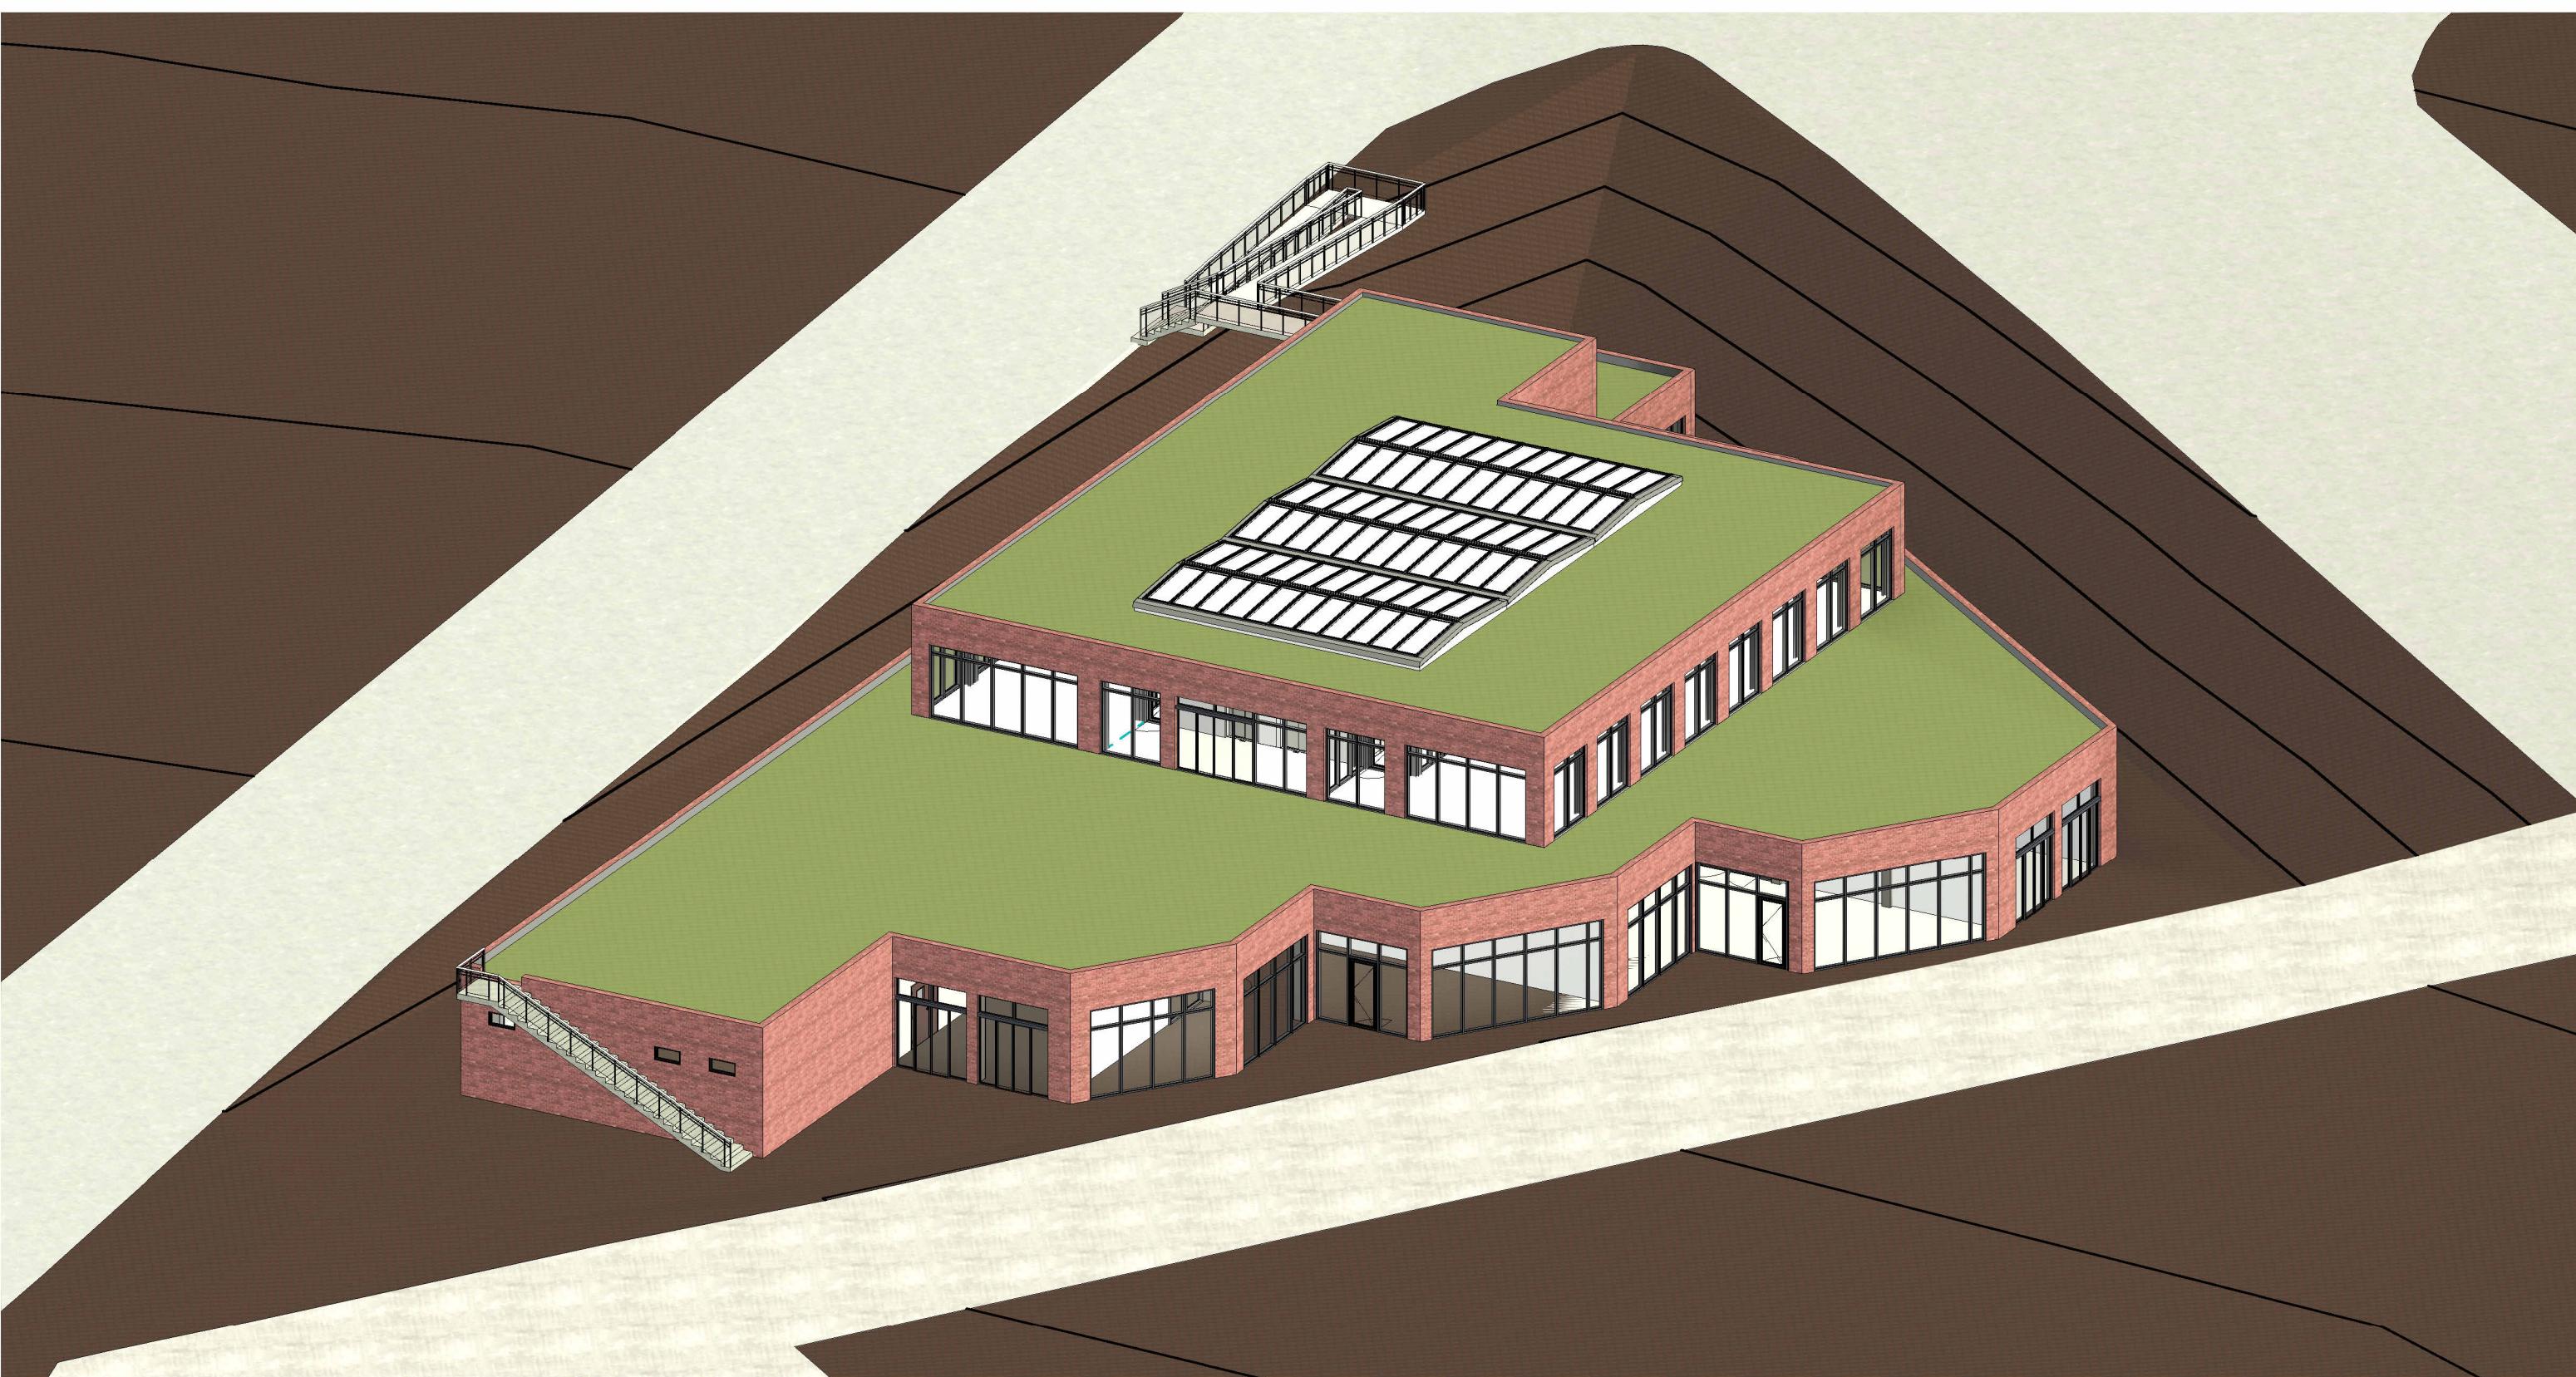

3D South

CODE	SUITABILITY DESCRIPTION
------	-------------------------

STATUS	PURPOSE OF ISSUE
--------	------------------

PROJECT

MSATD Major Design Project

TITLE

3D Views

CLIENT

Leeds City Council

DRAWN BY T Hermolle	CHECKED BY Checker	DATE 12/12/25
SCALE (@ A1)	PROJECT NUMBER Project Number	
DRAWING NUMBER A106	REV	